


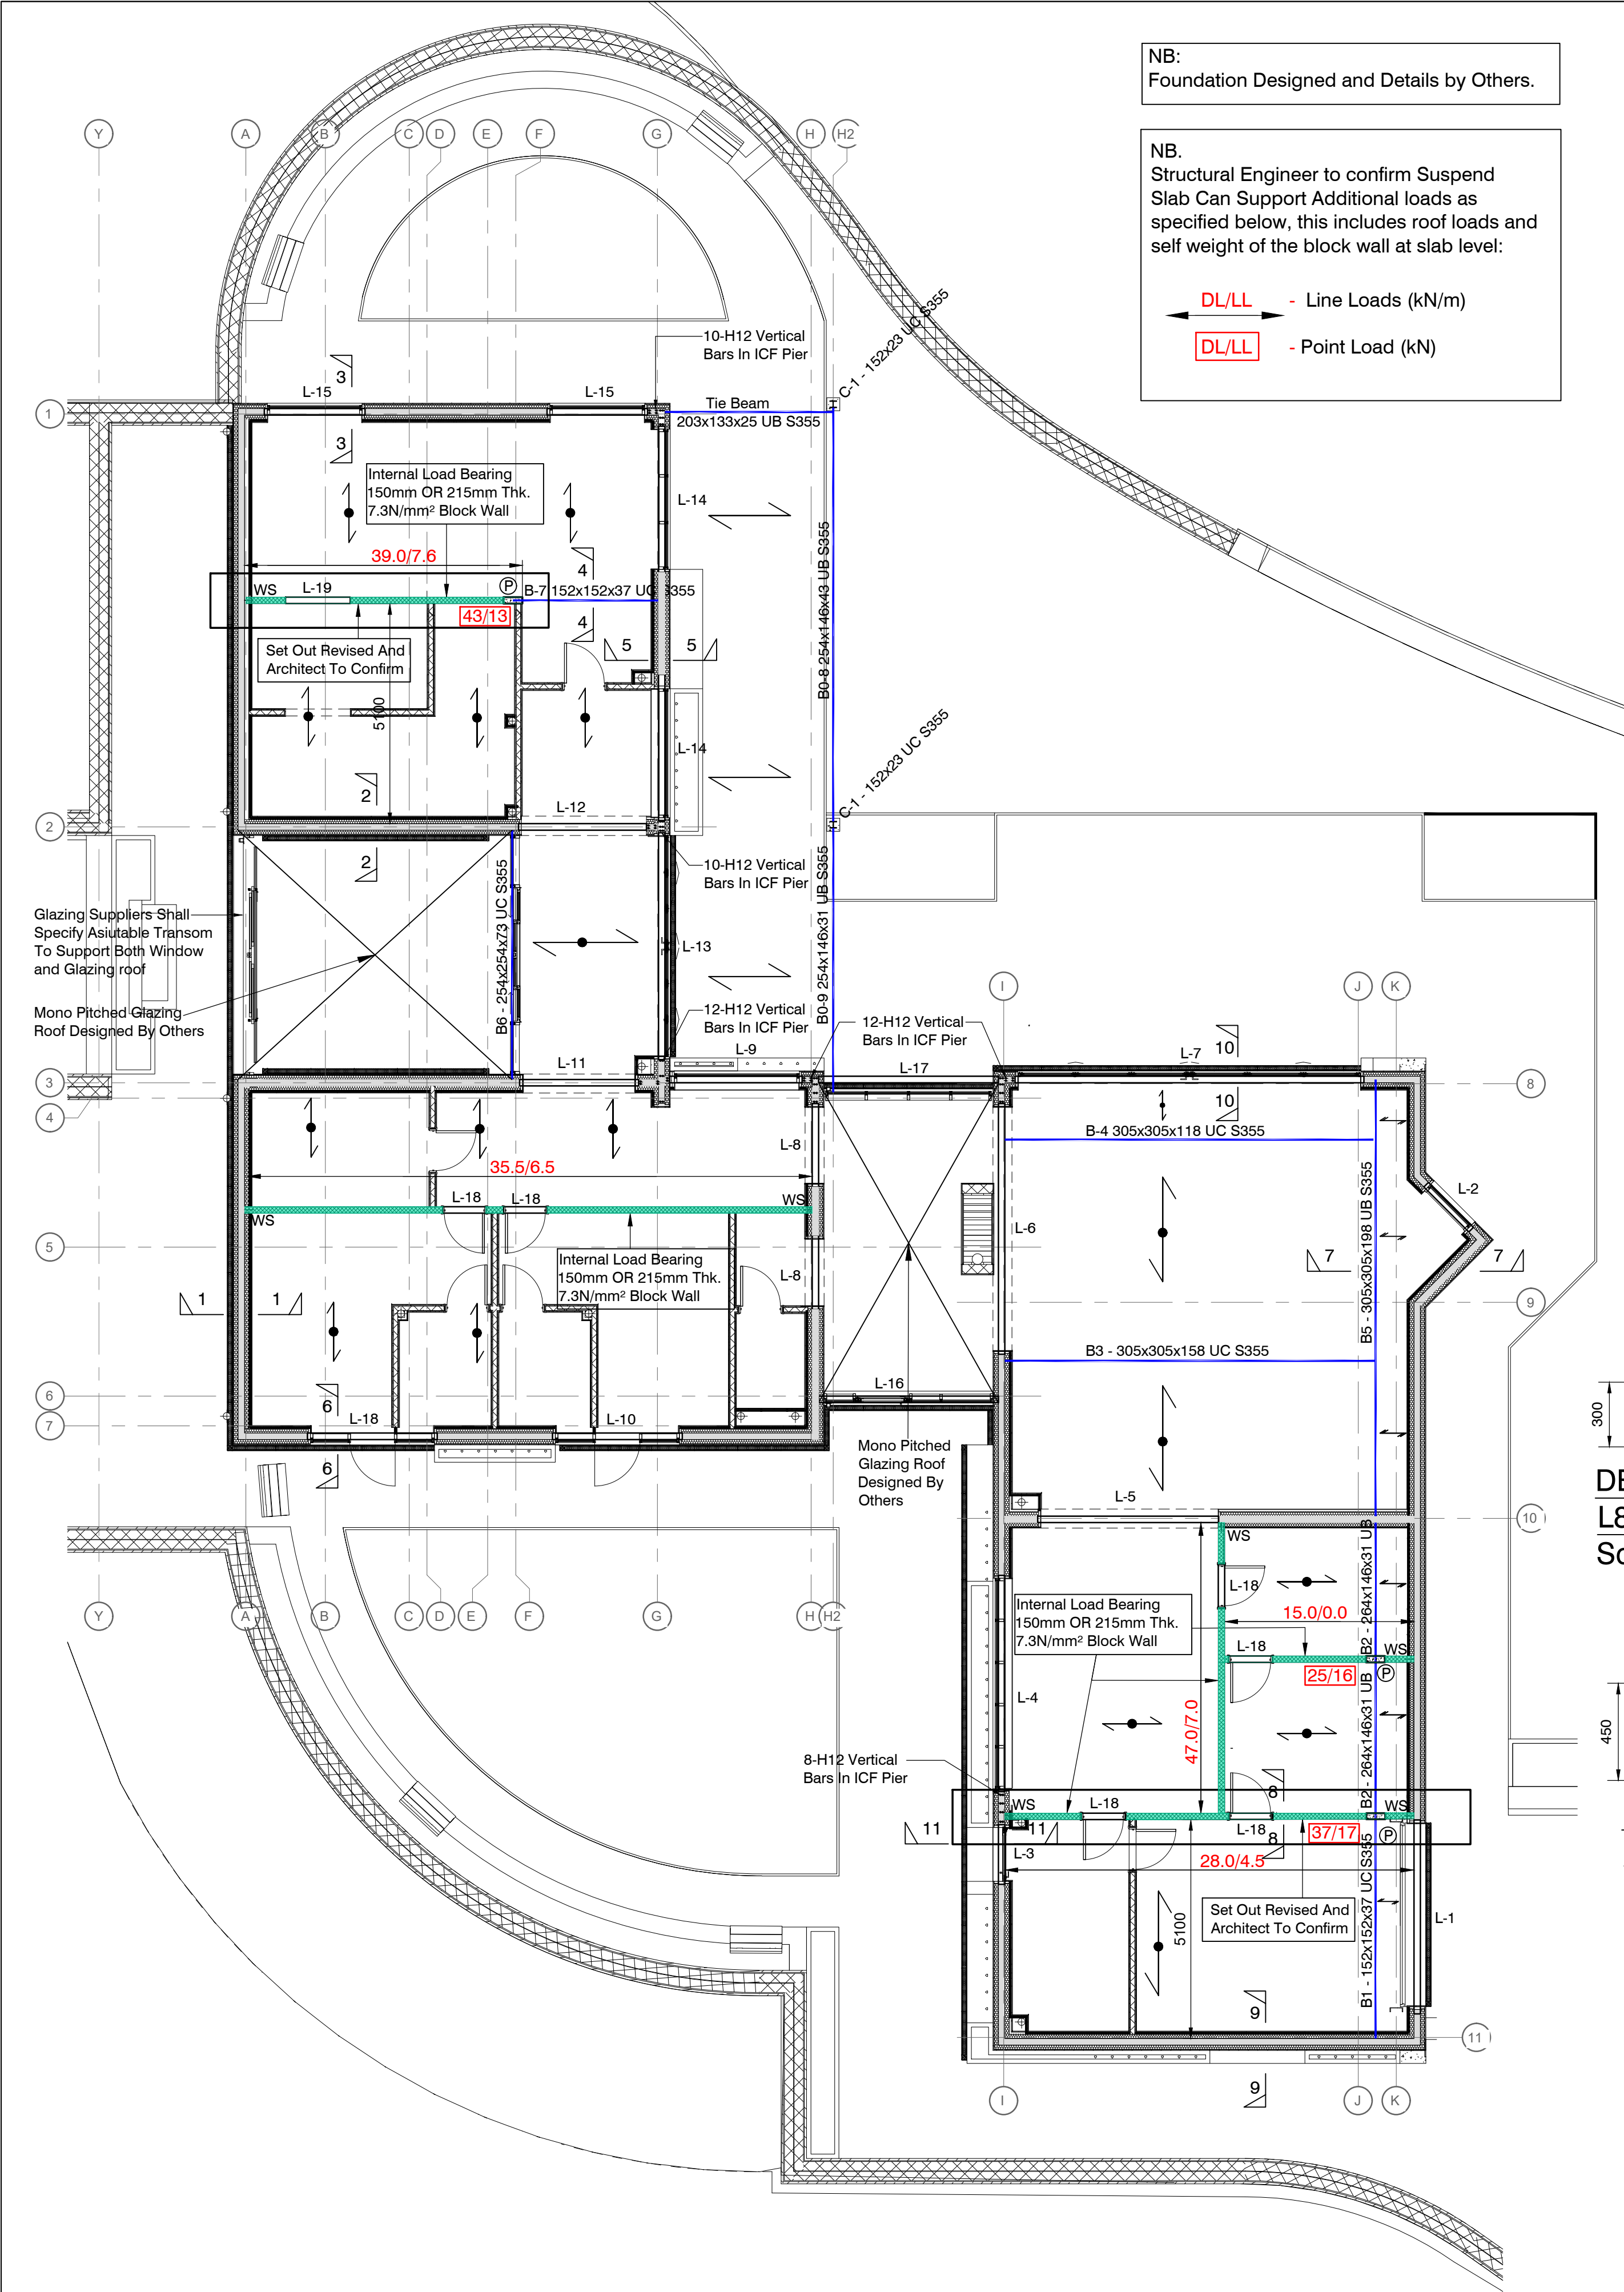

KEY	DESCRIPTION
EXT ICF150	150mm core ICF walls concrete grade C30, 10mm aggregate provide durus easy finish, polypropylene fibre reinforcement, dosage 2.5kg/m³ provide H16 dowel bars between lifts @ max 450mm c/c, 800mm long with 200mm embedment resin fixed
	Internal Load Bearing 150mm Thk. 7.3N/mm² Block Wall with Continuous Sheeting for the Comflor OR Alternatively 215mm thick 7.3N/mm² Block Wall with separate sheeting
	150mm thk comflor 80 Slab, C30 Concrete 1 Layer A193 mesh top OR 2.5kg/m³ Fibre dosage & H16 in troughs Bottom. Prop @ Midspan during pour for min 14 days
	47mmx220mm C24 @ 400mm c/c
	Timber Roof to specialist Supplier Design
WS	Wall Starters between ICF & Block Wall. Frame Cramps @ Max 225mm Vert. c/c.
P	C30 Precast Padstone 440x215x Width To Suit Wall

BEAM REF	BEAM SIZE
B - 1	152x152x37 UC S355 With 10mm Top Plate
B - 2	254x146x31 UB S355 With 10mm Top Plate & 200x100x10 Ledger Angle on one side
B - 3	305x305x158 UC S355 With 200x100x10mm Ledger Angles Both Sides
B - 4	305x305x118 UC S355 With 200x100x10mm Ledger Angle On Both Sides
B - 5	305x305x198 UC S355 With 200x100x10mm Ledger Angle On One Side only
B - 6	254x254x73 UC S355 With 200x100x10 Ledger Angle On One Side only OR For Concrete Option Similar Lintel 13 Details
B - 7	152x152x37 UC S355 With 10mm Bottom Plate Both sides
B - 8	254x146x43 UB S355
B - 9	254x146x31 UB S355
Tie Beam	203x133x25 UB S355

NB:
Construction/Fabrication Drawings To be checked by Structural Engineer prior to construction.


NB:
Waterproofing To Specialist Design.

LINTEL REF	TOTAL	DIMENSION HxW	REINFORCEMENT REQUIREMENT
L 1	1	300 x 150	2-H10 Bar top and 2-H12 Bar bott. H8 Links @ 200 c/c. RC30
L 2	1	300 x 150	1-H10 Bar top and 1-H12 Bar bott. H8 Links @ 200 c/c. RC30
L 3	1	300 x 150	1-H10 Bar top and 1-H12 Bar bott. H8 Links @ 200 c/c. RC30
L 4	1	450 x 150	2-H12 Bar top and 2-H20 Bar bott. H8 Links @ 200 c/c. RC30
L 5	1	450 x 150	2-H12 Bar top and 2-H16 Bar bott. H8 Links @ 200 c/c. RC30
L 6	1	450 x 150	2-H12 Bar top and 2-H20 + 2-H16 Bar bott. H10 Full Links @ 200 c/c. RC30 OR. Alternative 305x165x40UB S355
L 7	1	600 x 150	2-H12 Bar top and 2-H20 + 2-H16 Bar bott. H8 Links @ 200 c/c. RC30
L 8	2	300 x 150	2-H10 Bar top and 2-H12 Bar bott. H8 Links @ 200 c/c. RC30
L 9	1	300 x 150	2-H12 Bar top and 2-H16 Bar bott. H8 Links @ 200 c/c. RC30
L 10	1	300 x 150	2-H12 Bar top and 2-H16 Bar bott. H8 Links @ 200 c/c. RC30
L 11	1	300 x 150	2-H10 Bar top and 2-H12 Bar bott. H8 Links @ 200 c/c. RC30
L 12	1	450 x 150	2-H12 Bar top and 2-H16 Bar bott. H8 Links @ 200 c/c. RC30
L 13	1	600 x 150 450 x 150	2-H12 Bar top and 2-H20 Bar bott. H8 Links @ 200 c/c. RC30 OR L-13 Option 2 2-H12 Bar top and 2-H20 + 2-H16 Bar bott. H10 Links @ 200 c/c. RC30
L 14	2	300 x 150	2-H10 Bar top and 2-H12 Bar bott. H8 Links @ 200 c/c. RC30
L 15	2	300 x 150	2-H10 Bar top and 2-H12 Bar bott. H8 Links @ 200 c/c. RC30
L 16	1	300 x 150	2-H12 Bar top and 2-H16 Bar bott. H8 Links @ 200 c/c. RC30
L 17	1	300 x 150	2-H12 Bar top and 2-H20 Bar bott. H8 Links @ 200 c/c. RC30
L 18	6		Concrete Pre-cast Lintel by Naylor Ref: R8 (140 x 215) for 140mm block wall OR. Concrete Pre-cast Lintel by Naylor Ref: R7 (215 x 145) for 215mm block wall
L 19	1		Concrete Pre-cast Lintel by Naylor Ref: R8 (140 x 215) for 140mm block wall OR. Concrete Pre-cast Lintel by Naylor Ref: S8 (215 x 215) for 215mm block wall


COLN REF	COLUMN SIZE
C-1	152x152x23 UC S355

Provide temporary propping to the bottom plate where it provide to support Comflor at the third points of the beam until the floor concrete has achieved its required strength.


NB:
Levels, setting out, insulation & finishes to architects specification and details.

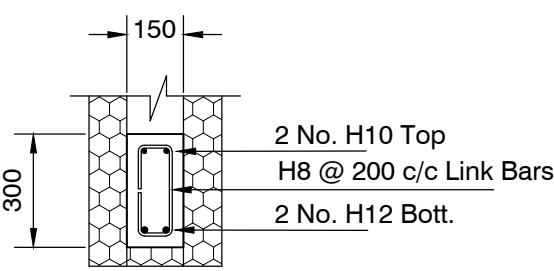


DETAIL RC LINTEL - L1, L8, L11, L14 & L15
Scale 1:20

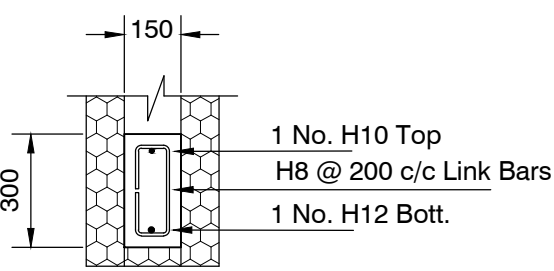


DETAIL RC LINTEL - L2 & L3
Scale 1:20

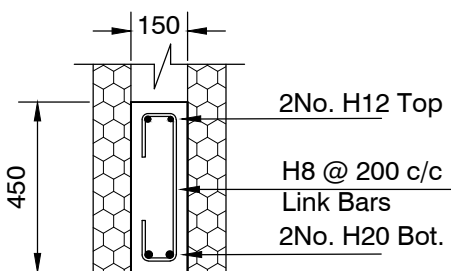


DETAIL RC LINTEL - L4
Scale 1:20

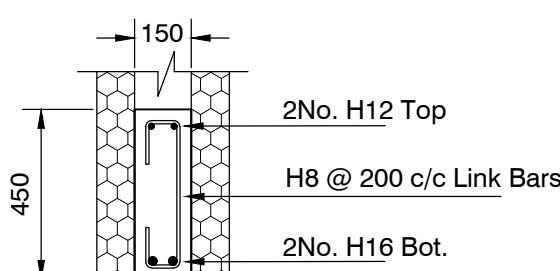


DETAIL RC LINTEL - L5 & L12
Scale 1:20

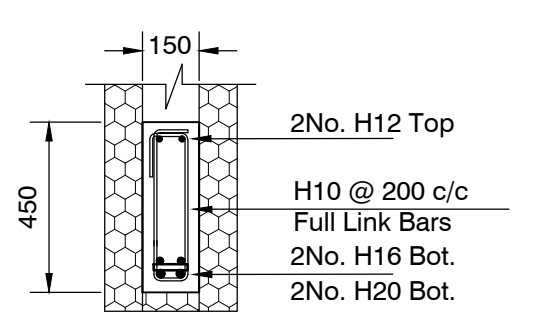


DETAIL RC LINTEL - L6
Scale 1:20

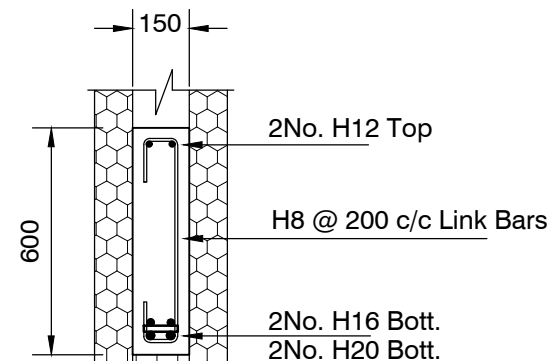


DETAIL RC LINTEL - L7
Scale 1:20

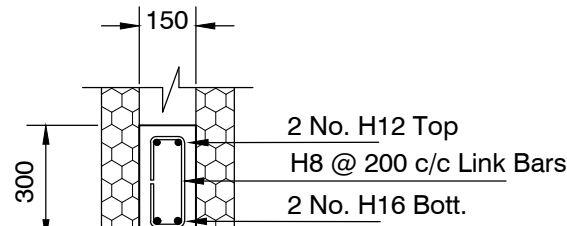


DETAIL RC LINTEL - L9 & L10
Scale 1:20

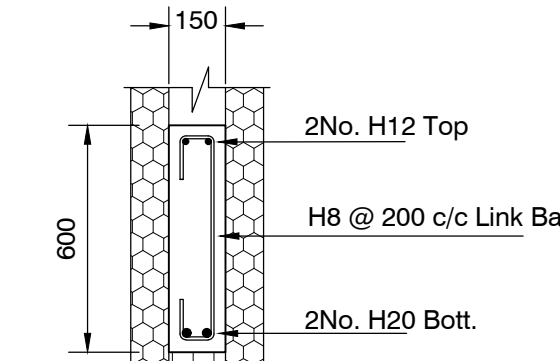

DETAIL RC LINTEL - L13
Scale 1:20

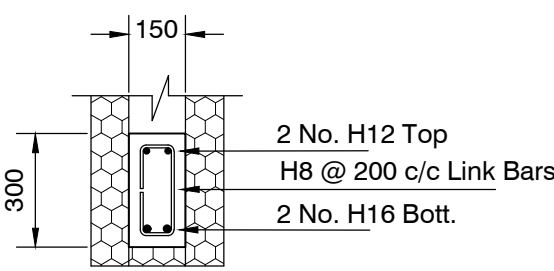

DETAIL RC LINTEL L - 16
Scale 1:20

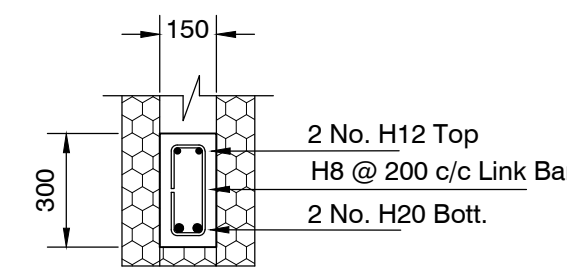

DETAIL RC LINTEL - L17
Scale 1:20

NOTES:

GENERAL NOTES:-

- THIS DRAWING IS TO BE READ IN CONJUNCTION WITH ALL OTHER RELEVANT CARB ZERO CONSULTANTS, ARCHITECT'S AND SPECIALIST'S DRAWINGS AND ANY SPECIFICATIONS. ANY DISCREPANCIES FOUND BETWEEN THESE DRAWINGS, BY THE CONTRACTOR, SHOULD BE REPORTED IMMEDIATELY AND PRIOR TO THE INITIATION OF ANY AFFECTED WORK ON SITE.
- THIS DRAWING IS NOT TO BE SCALED.
- THE CONTRACTOR SHALL CHECK ALL DIMENSIONS AND LEVELS ON SITE

STEELWORK NOTES:-

- ALL STRUCTURAL STEELWORK INCLUDING BOLTS, CLEATS ETC, TO BE SUPPLIED BY THE STEELWORK SUB-CONTRACTOR ALL IN ACCORDANCE WITH STRUCTURAL STEELWORK SPECIFICATION G10.
- ALL STRUCTURAL STEELWORK TO BE MILD STEEL GRADE S355 UNLESS NOTED OTHERWISE.
- ALL BOLTS TO BE M16 DIA. BOLTS GRADE 8.8 U.N.O.
- ALL WELDS TO BE 6mm CONTINUOUS FILLET WELD U.N.O.
- ALL PLATES TO BE 15mm THICK MINIMUM U.N.O.
- ALL MEMBERS TO HAVE A MINIMUM OF TWO BOLT CONNECTIONS. ALL BEAMS TO HAVE A MINIMUM OF FOUR BOLT CONNECTIONS.
- END CONNECTIONS TO BE DESIGNED BY THE STEELWORK SUB-CONTRACTOR SUBJECT TO THE MINIMA COVERED IN NOTES 2 TO 6 ABOVE AND TO MEET THE REQUIREMENTS OF BS: 5950. COPIES OF THESE CALCULATIONS ARE TO BE SUBMITTED TO FORWARD STRUCTURAL CONSULTANTS FOR EXAMINATION.
- THE STEELWORK SUB-CONTRACTOR SHALL BE RESPONSIBLE FOR TAKING ALL NECESSARY SITE MEASUREMENTS OF THE EXISTING BUILDINGS WHEN REQUIRED, PRIOR TO FABRICATION TO ENSURE THE CORRECT FIT OF THE NEW WORKS ON SITE.
- THE STEELWORK SUB-CONTRACTOR SHALL BE RESPONSIBLE FOR THE STABILITY OF THE STRUCTURE DURING ERECTION AND SHALL PROVIDE ANY TEMPORARY BRACINGS AS NECESSARY.
- ALL STEEL TO BE SUPPLIED IN ACCORDANCE WITH EXECUTION CLASS 2

REV	DESCRIPTION	DATE	BY	TH
C	AMENDED TO CLIENTS INSTRUCTIONS	10/09/26	E.P	TH
B	AMENDED TO ARCHITECTS DRAWINGS	08/09/26	E.P	TH
A	ISSUED FOR COMMENTS	06/08/26	E.P	TH

REF REVISIONS SHOWN THUS DATE BY AUTH

Carb Zero Consultants
Consulting Civil & Structural Engineers
Bloxham Mill
Barford Road
Bloxham, Banbury, Oxon
Tel 01295 722805
timh@carbzero.co.uk

CLIENT
MR A KIRKPATRICK

PROJECT
**HORROBIN FARM TURTON
LANCASHIRE BL7-0FW**

TITLE
**GROUND FLOOR PLAN SHOWING
ROOF STRUCTURE ABOVE**

DRAWN	AUTHORISED	SCALE	REV
E.P	TH	1:100, 1:20	
DATE	PROJECT NO.	DRAWING NO.	
AUG 26	26-92	01	C