



FOR APPROVAL - NOT FOR CONSTRUCTION

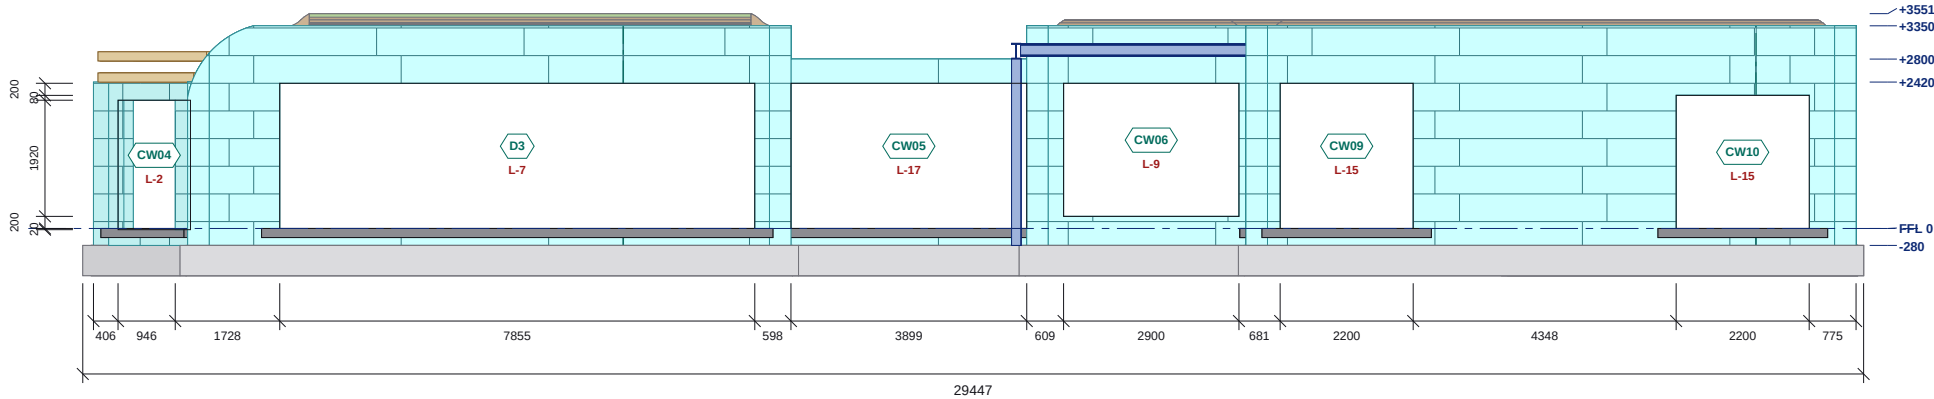


NORTH ELEVATION

Scale 1:125 @ A3 | Levels above GF FFL (AOD in the schedule); left: sills and heads on this face

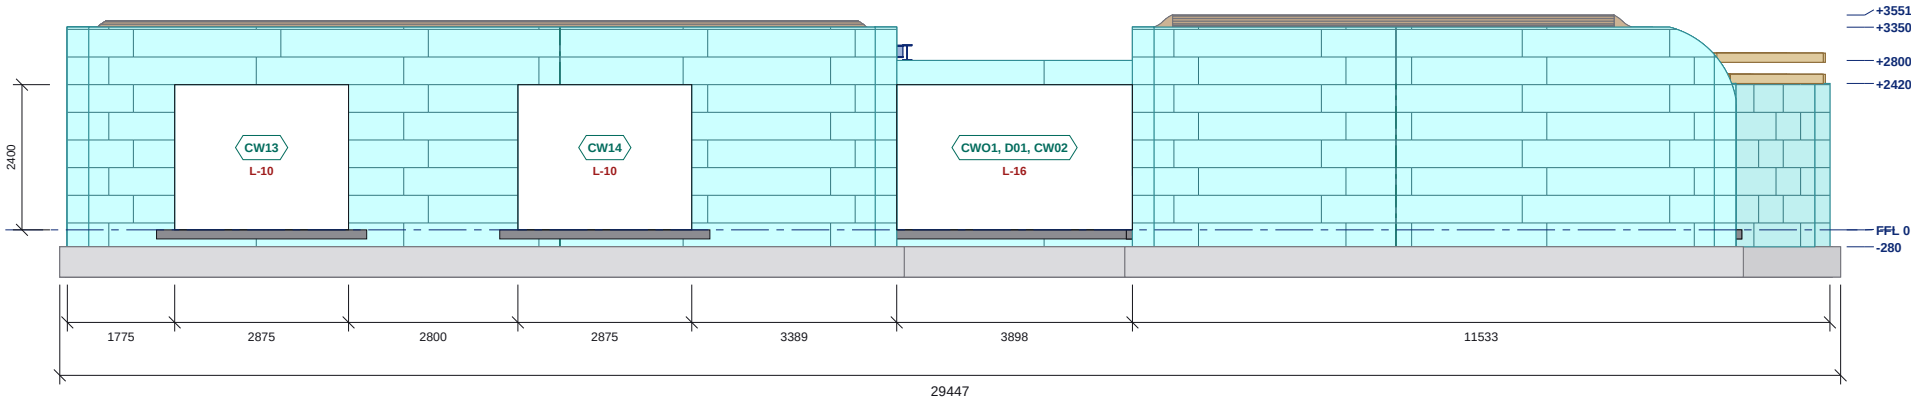

SOUTH ELEVATION

Scale 1:125 @ A3 | Levels above GF FFL (AOD in the schedule); left: sills and heads on this face

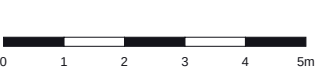

- ICF external EPS face
- Block course joint
- Stack joint
- Steel
- Roof build-up (slab / earth / sedum)
- Curved trusses / timbers
- GF slab + foundation build-up, ACO

ELEVATION SCHEDULES

NORTH ELEVATION: OPENINGS

Ref	Width	Height	Sill	Head	Lintel
CW04 (1)	1338	2140	-20	+2120	L-2
CW05	3899	2400	0	+2400	L-17
CW06	2900	2200	+200	+2400	L-9
CW09	2200	2400	0	+2400	L-15
CW10	2200	2200	0	+2200	L-15
D3	7855	2400	0	+2400	L-7

Structural openings in the ICF; sill and head above GF FFL. (1) CW04: head lowered from +2355 to take L-2 (300) under the +2420 wall top.

SOUTH ELEVATION: OPENINGS

Ref	Width	Height	Sill	Head	Lintel
CW01, D01, CW02	3898	2400	0	+2400	L-16
CW13	2875	2400	0	+2400	L-10
CW14	2875	2400	0	+2400	L-10

Structural openings in the ICF; sill and head above GF FFL.

NORTH ELEVATION: LEVELS

Level	FFL	AOD
underside of ICF	-280	143.470
GF FFL	0	143.750
top of ICF	+2420	146.170
top of ICF	+2800	146.550
top of ICF	+3350	147.100
top of roof build-up	+3551	147.301

SOUTH ELEVATION: LEVELS

Level	FFL	AOD
underside of ICF	-280	143.470
GF FFL	0	143.750
top of ICF	+2420	146.170
top of ICF	+2800	146.550
top of ICF	+3350	147.100
top of roof build-up	+3551	147.301

NOTES

- ICF: Nudura 6" XR35 (101.6 EPS + 152.4 core + 101.6 EPS = 355.6). External EPS face shown with the block course joints, vertical block joints and stack joints as populated.
- Levels above GF FFL (143.750 AOD). Openings are structural openings in the ICF; glazing, doors, render and finishes by others, not shown.
- Roof build-up, steel, curved trusses, GF slab / foundation build-up (BR11) and ACO drains shown as modelled.
- See UKPCS-002-GA-01 for plan setting out, lintels and steel.

REVISIONS

REV	DATE	DESCRIPTION
P01	14.09.26	Approval issue
P02	15.09.26	CW13 lintel L-18 revised to L-10 (engineer, EQ-01 closed)



CLIENT	PROJECT
Mr A Kirkpatrick	11767 Horrobin Farm, Turton

DRAWING TITLE

NORTH AND SOUTH ELEVATIONS

ICF elevations with openings, levels and roof build-up

SCALE	SIZE	DATE	DRAWN
1:125	A3	15.09.26	TS

STATUS	DRAWING No.	REV
FOR APPROVAL	UKPCS-002-EL-01	P02