



FOR APPROVAL - NOT FOR CONSTRUCTION

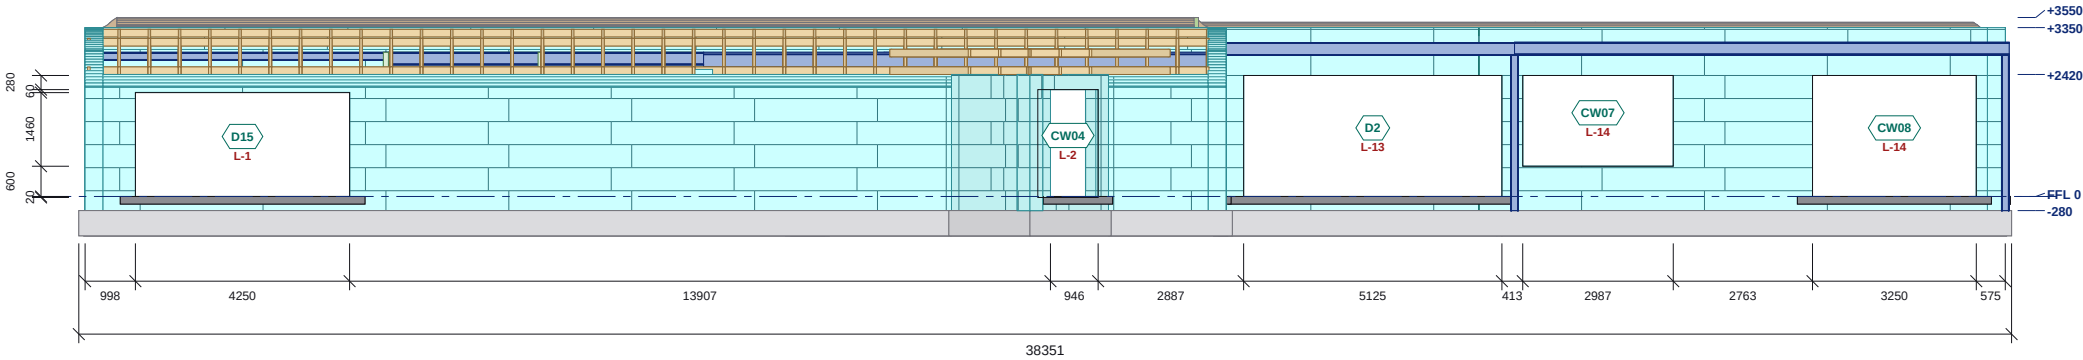


### EAST ELEVATION

Scale 1:150 @ A3 | Levels above GF FFL (AOD in the schedule); left: sills and heads on this face

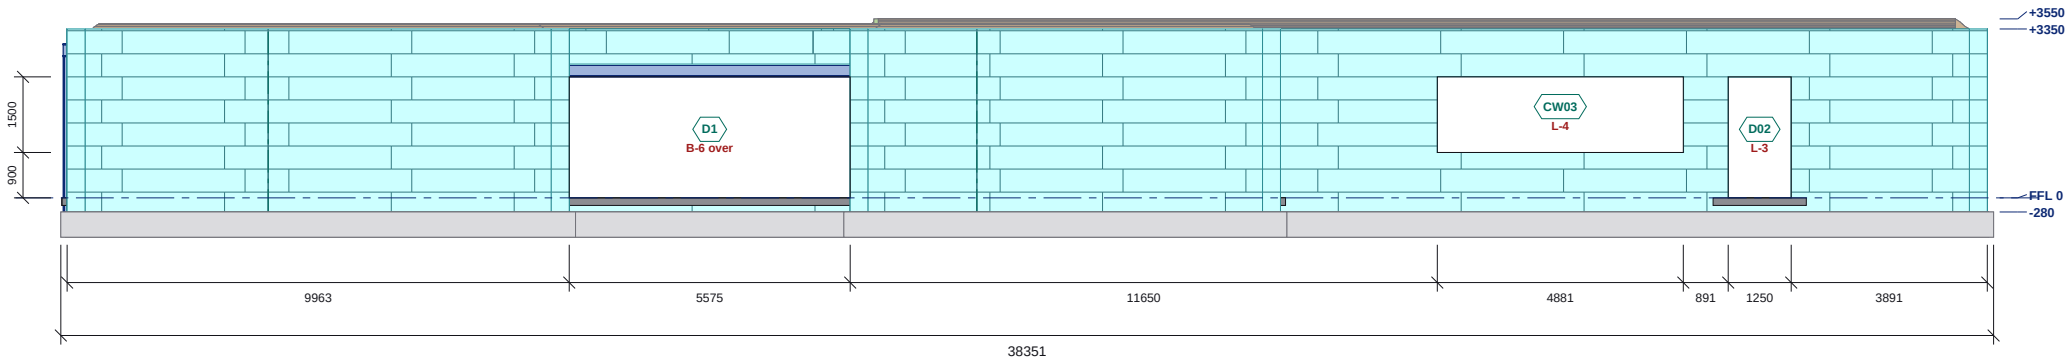

### WEST ELEVATION

Scale 1:150 @ A3 | Levels above GF FFL (AOD in the schedule); left: sills and heads on this face

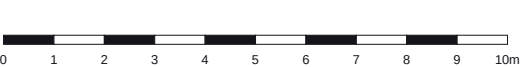

- ICF external EPS face
- Block course joint
- Stack joint
- Steel
- Roof build-up (slab / earth / sedum)
- Curved trusses / timbers
- GF slab + foundation build-up, ACO

### ELEVATION SCHEDULES

#### EAST ELEVATION: OPENINGS

| Ref      | Width | Height | Sill | Head  | Lintel |
|----------|-------|--------|------|-------|--------|
| CW04 (1) | 1338  | 2140   | -20  | +2120 | L-2    |
| CW07     | 2987  | 1800   | +600 | +2400 | L-14   |
| CW08     | 3250  | 2400   | 0    | +2400 | L-14   |
| D2       | 5125  | 2400   | 0    | +2400 | L-13   |
| D15      | 4250  | 2060   | 0    | +2060 | L-1    |

Structural openings in the ICF; sill and head above GF FFL. (1) CW04: head lowered from +2355 to take L-2 (300) under the +2420 wall top.

#### WEST ELEVATION: OPENINGS

| Ref    | Width | Height | Sill | Head  | Lintel   |
|--------|-------|--------|------|-------|----------|
| CW03   | 4881  | 1500   | +900 | +2400 | L-4      |
| D1 (3) | 5575  | 2400   | 0    | +2400 | B-6 over |
| D02    | 1250  | 2400   | 0    | +2400 | L-3      |

Structural openings in the ICF; sill and head above GF FFL. (3) D1: height = clear under B-6 (BOS +2400); ICF open to +2654 with B-6 in the head (EQ-02).

#### EAST ELEVATION: LEVELS

| Level                | FFL   | AOD     |
|----------------------|-------|---------|
| underside of ICF     | -280  | 143.470 |
| GF FFL               | 0     | 143.750 |
| top of ICF           | +2420 | 146.170 |
| top of ICF           | +3350 | 147.100 |
| top of roof build-up | +3550 | 147.300 |

#### WEST ELEVATION: LEVELS

| Level                | FFL   | AOD     |
|----------------------|-------|---------|
| underside of ICF     | -280  | 143.470 |
| GF FFL               | 0     | 143.750 |
| top of ICF           | +3350 | 147.100 |
| top of roof build-up | +3550 | 147.300 |

### NOTES

- ICF: Nudura 6" XR35 (101.6 EPS + 152.4 core + 101.6 EPS = 355.6). External EPS face shown with the block course joints, vertical block joints and stack joints as populated.
- Levels above GF FFL (143.750 AOD). Openings are structural openings in the ICF; glazing, doors, render and finishes by others, not shown.
- Roof build-up, steel, curved trusses, GF slab / foundation build-up (BR11) and ACO drains shown as modelled.
- See UKPCS-002-GA-01 for plan setting out, lintels and steel.

### REVISIONS

| REV | DATE     | DESCRIPTION    |
|-----|----------|----------------|
| P01 | 14.09.26 | Approval issue |



|                  |                             |
|------------------|-----------------------------|
| CLIENT           | PROJECT                     |
| Mr A Kirkpatrick | 11767 Horrobin Farm, Turton |

### DRAWING TITLE

#### EAST AND WEST ELEVATIONS

ICF elevations with openings, levels and roof build-up

|       |      |          |       |
|-------|------|----------|-------|
| SCALE | SIZE | DATE     | DRAWN |
| 1:150 | A3   | 14.09.26 | TS    |

|              |                 |     |
|--------------|-----------------|-----|
| STATUS       | DRAWING No.     | REV |
| FOR APPROVAL | UKPCS-002-EL-02 | P01 |