


OPTION B - FOR APPROVAL - NOT FOR CONSTRUCTION

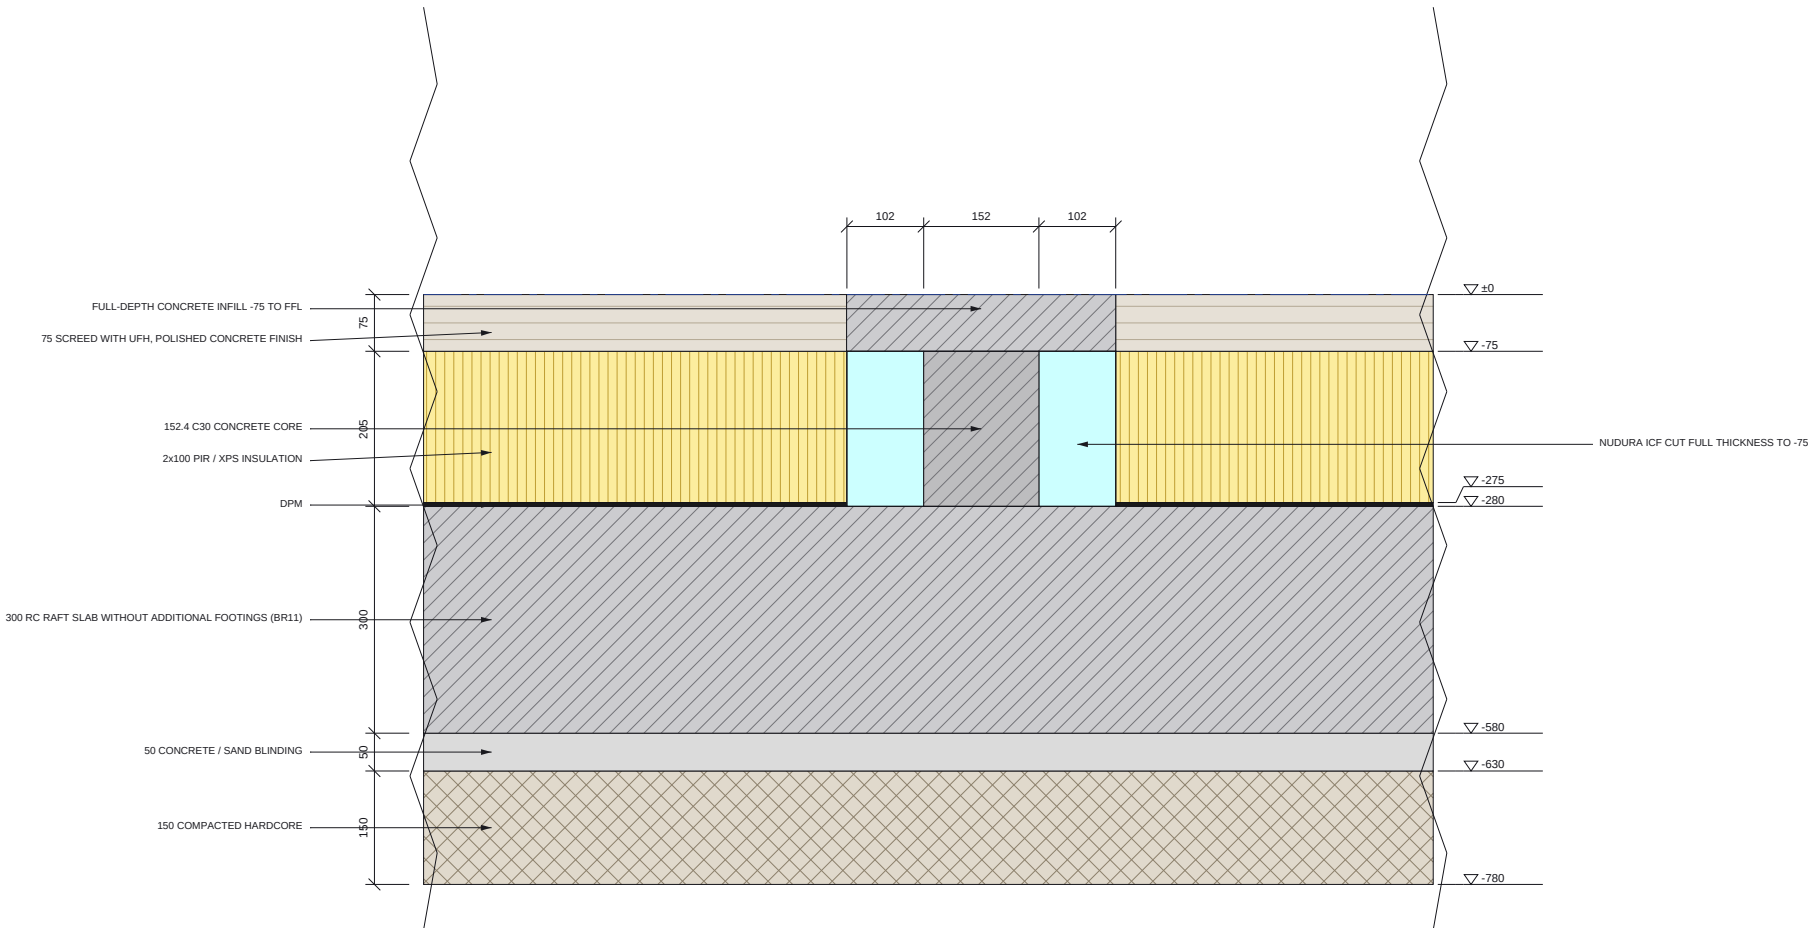

THRESHOLD DETAIL - INTERNAL SCHEDULE

OPENINGS WITH THIS THRESHOLD

Ref	Width	Sill	Head	Lintel
D13	1587	0	+2400	L-8
D14	1800	0	+2400	L-8
D4	5675	0	+2400	L-6
VOID W19	4143	0	+2070	L-5
VOID W4	2887	0	+2400	L-12
VOID W7	2400	0	+2400	L-11

Structural openings; sill and head above GF FFL. VOID = subtract cut in the ICF (no end caps).

LEVELS IN THIS DETAIL

Level	FFL	AOD
underside of hardcore	-780	142.970
underside of blinding	-630	143.120
underside of raft	-580	143.170
underside of ICF / top of RC raft	-280	143.470
DPM / top of raft	-275	143.475
ICF cut / top of insulation / threshold infill	-75	143.675
GF FFL / top of screed	0	143.750

NOTES

- Threshold detail cut square to the wall through D4; applies to every opening listed (same threshold type).
- Internal threshold between building sections: ICF cut full thickness to -75, full-depth concrete infill -75 to FFL, no ACO.
- Architect's threshold note (BR11 / BR12 / BR13): "Rebated curtain wall framing to suit level of access. PPC aluminium flashing to threshold. Below FFL ICF block 200mm high." Door / curtain wall frame, flashing and finishes by others, not shown.
- Ground floor build-up BR11. Levels above GF FFL (143.750 AOD). ICF Nudura 6" XR35; no lintel closure / bottom buck at internal thresholds.

REVISIONS

REV	DATE	DESCRIPTION
P01	15.09.26	Approval issue - Option B: external ICF 100mm in from slab edge

CLIENT	PROJECT
Mr A Kirkpatrick	11767 Horrobin Farm, Turton

DRAWING TITLE
THRESHOLD DETAIL - INTERNAL

SCALE	SIZE	DATE	DRAWN
1:10	A3	15.09.26	TS

STATUS

FOR APPROVAL

DRAWING No.

UKPCS-002-DT-02B

REV

P01

THRESHOLD DETAIL - INTERNAL (AT D4)

Scale 1:10 @ A3 | Section square to the wall through the opening

